


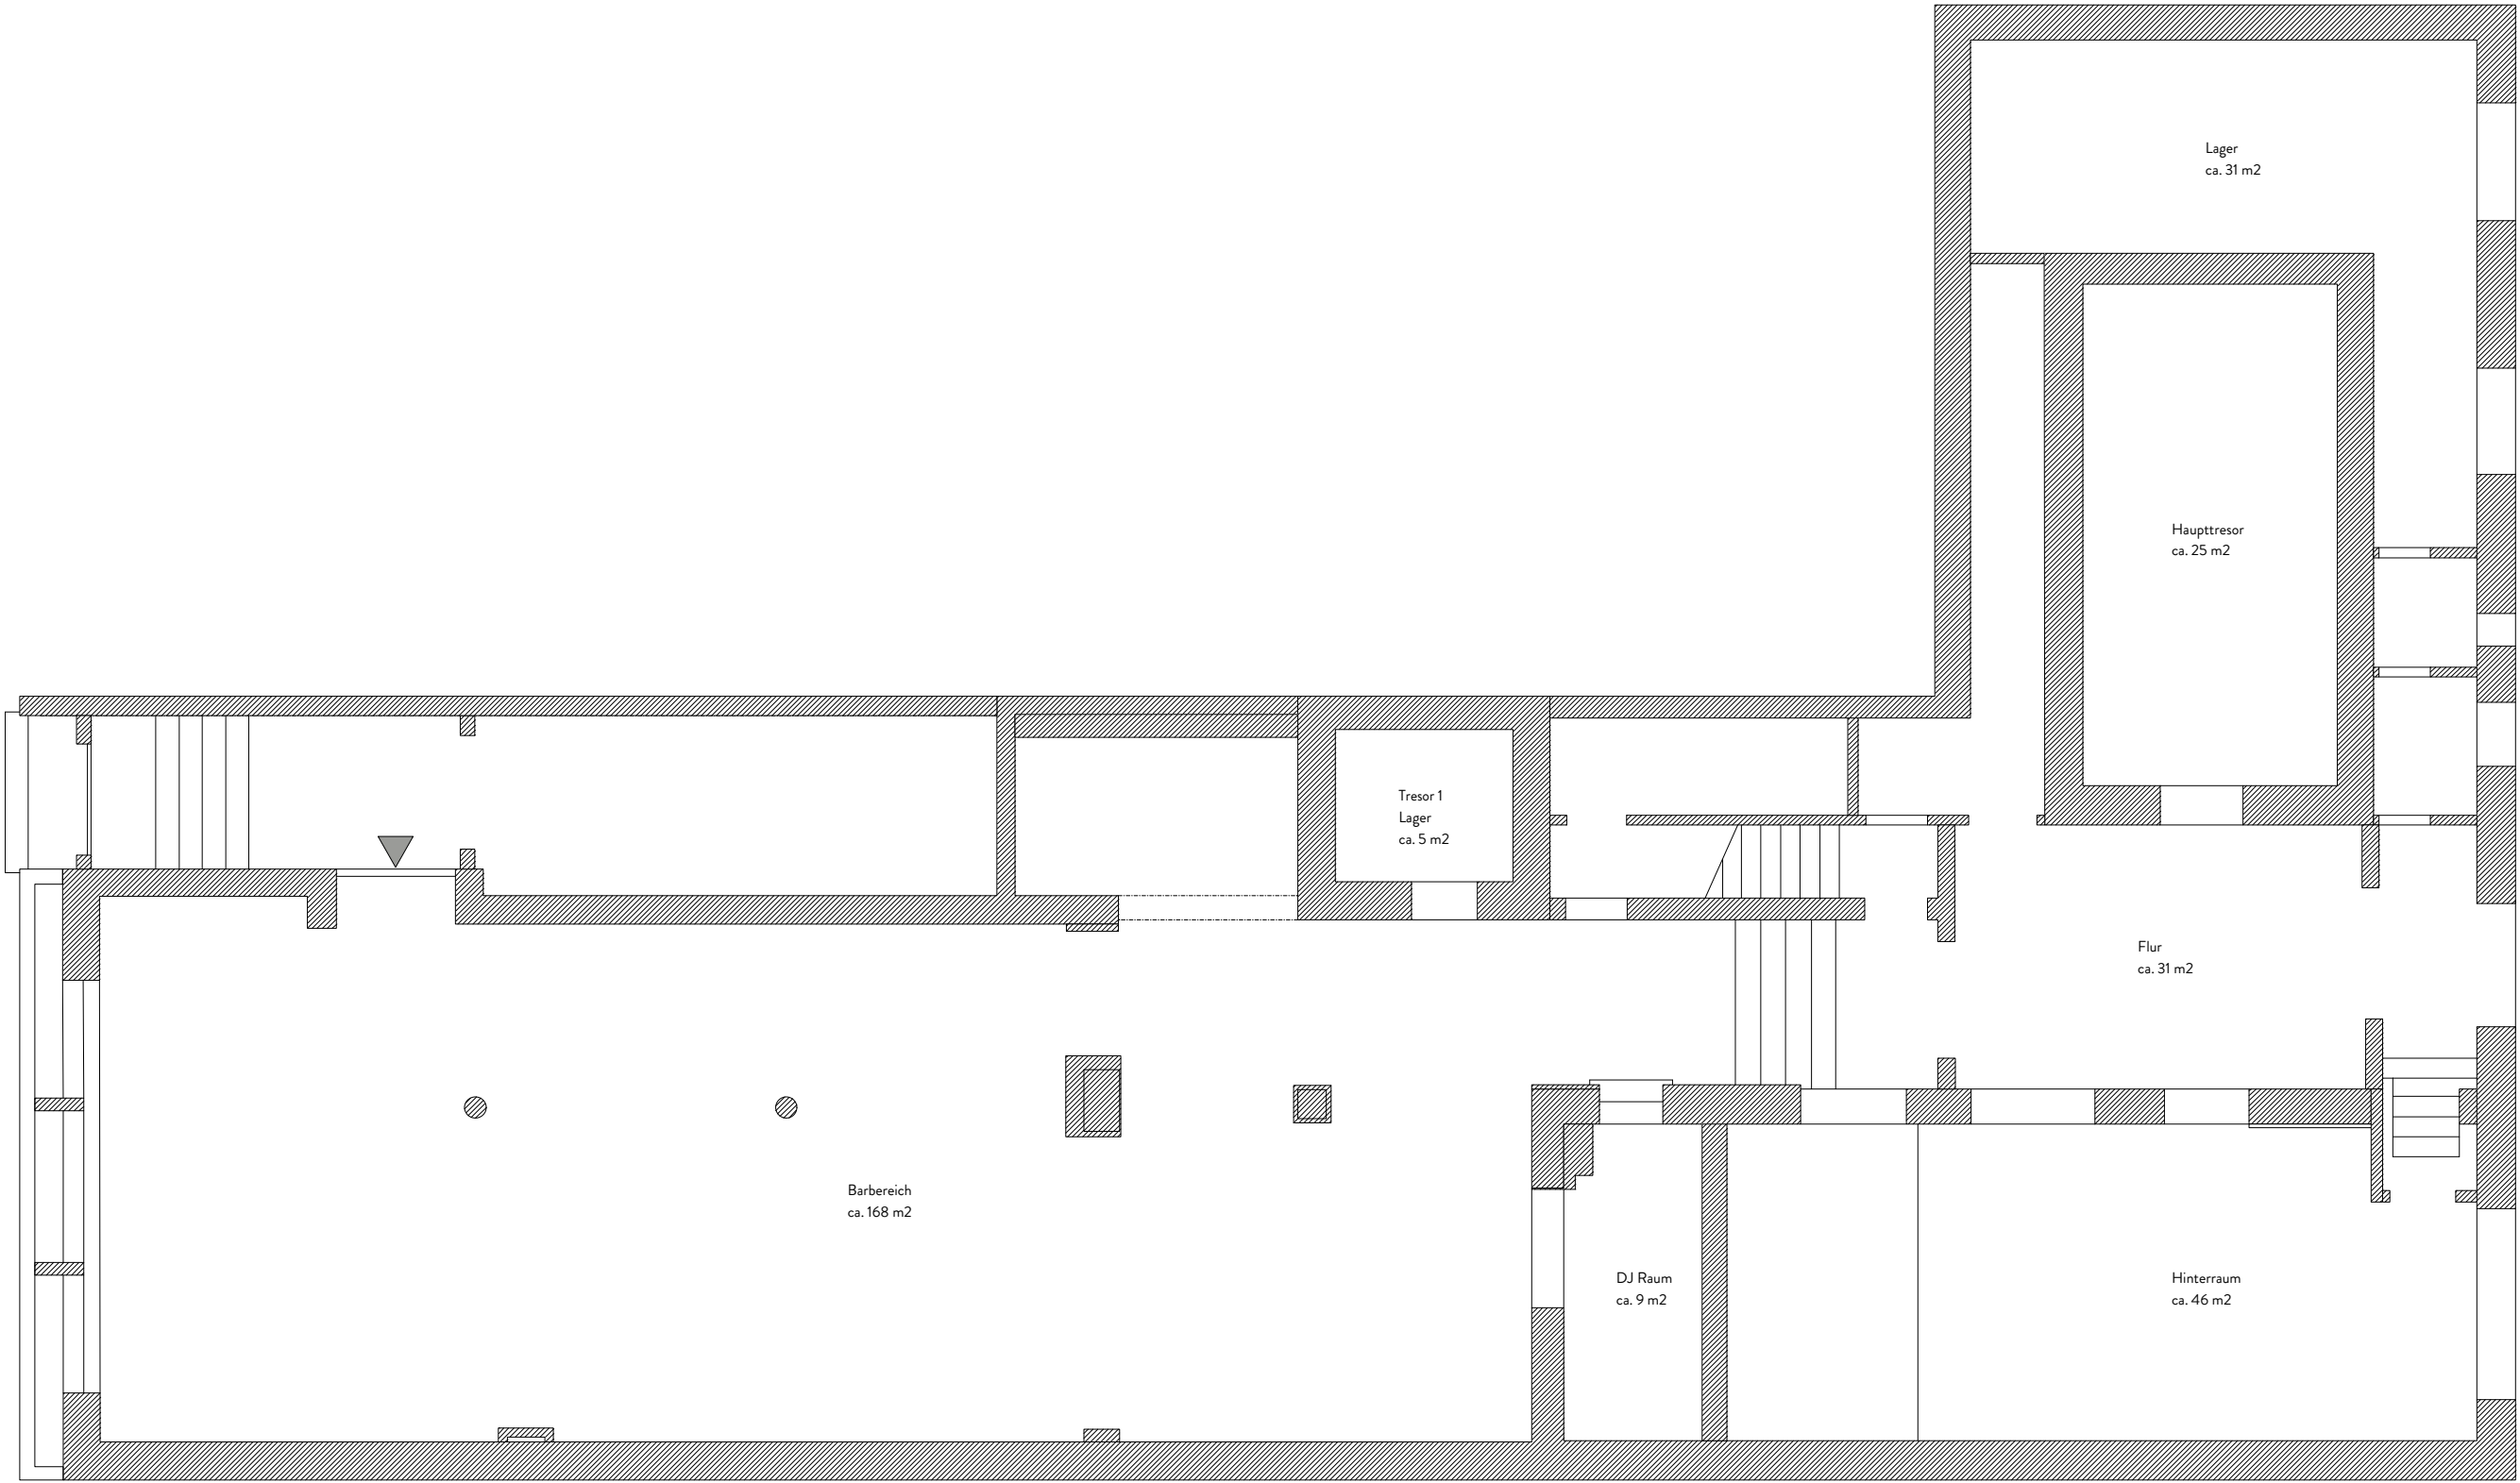

ANMERKUNGEN			
A	Bestand geprüft & angepasst	29.7.20	osh
INDEX	KOMMENTAR	DATUM	GEZ.
BEMERKUNG			
Alle Maße sind vor Beginn der Arbeiten vom Auftragnehmer vor Ort zu prüfen! Bei Unklarheiten und Maßdifferenzen ist sofort die Bauleitung zu benachrichtigen.			

PROJEKT		409	Pallas	
Neuer Pferdemarkt 13, 20359 Hamburg				
BEZEICHNUNG				
EG_GR_Bestand				
PLANNR.		INDEX		DATUM
0EG_010		0		29.07.2020
FORMAT	A2	MASSTAB	1:100	GEZEICHNET osh
DATEI				
409_Pallas.vwx				
PLANSTATUS				
VORABZUG				
LEISTUNGSPHASE				
Vorplanung				
FACHPLANER				
BAUHERR				
PLANER				
 BFGF DESIGN STUDIOS Lippmannstrasse 53-55, 22769 Hamburg Telefon: (040) 31 78 70-0 Fax: (040) 31 04 29				